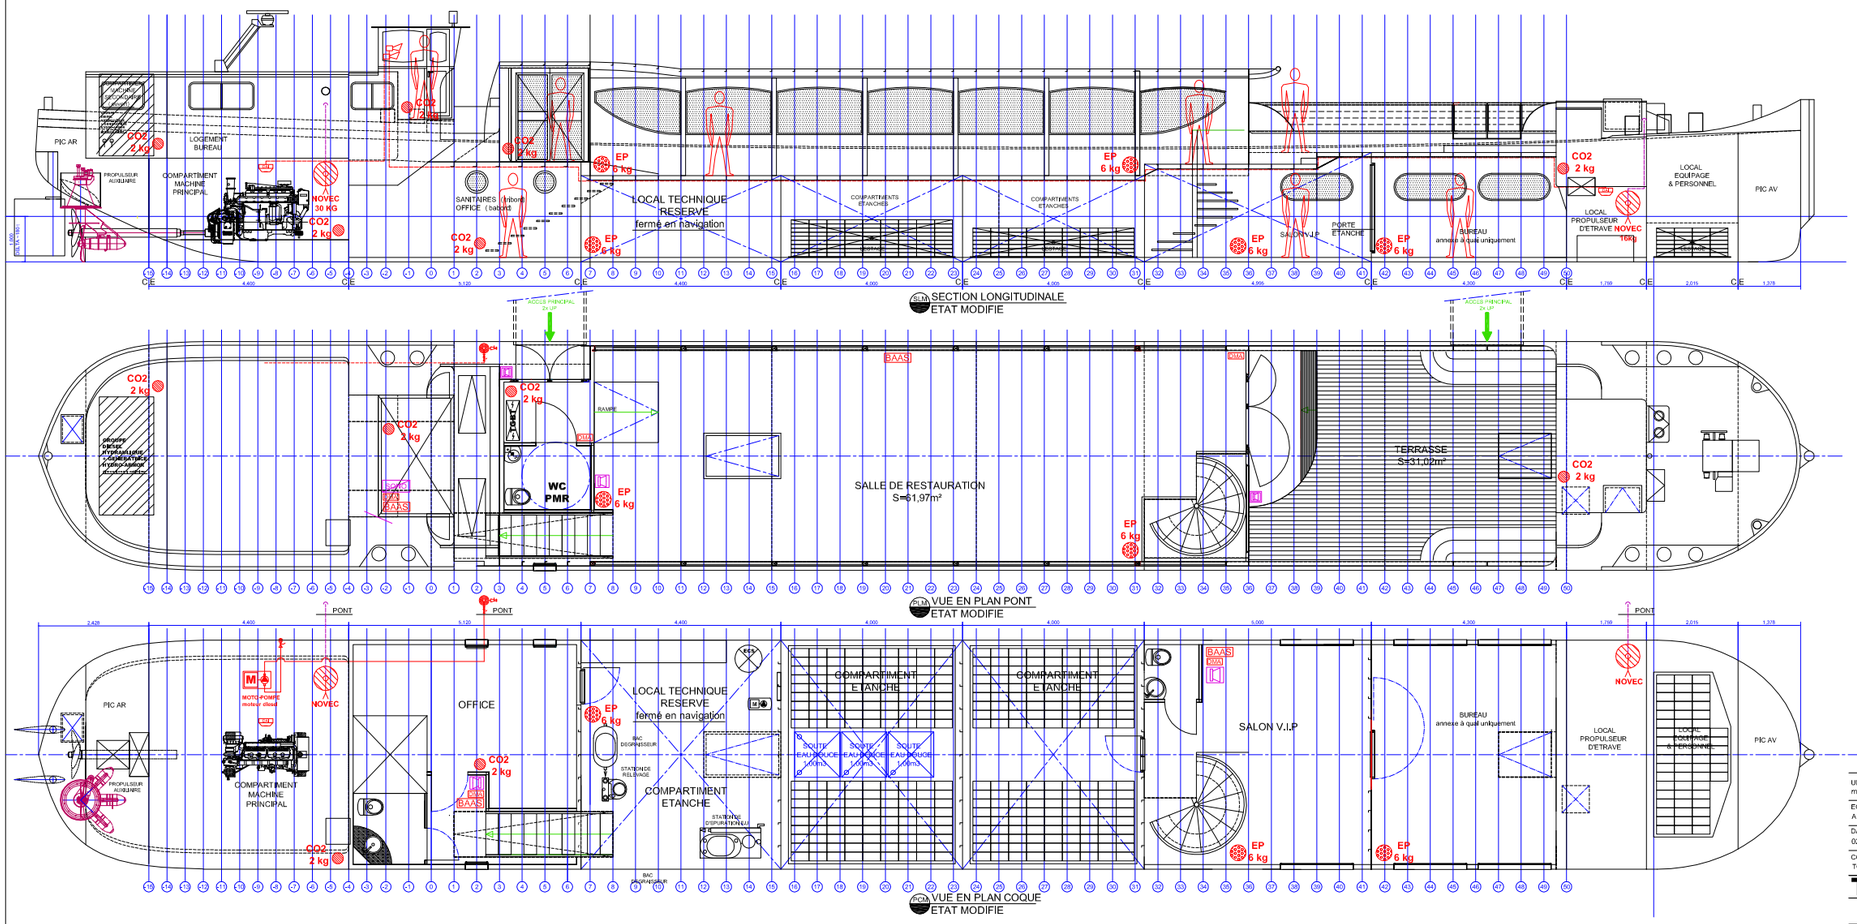



## EQUIPEMENTS DE SONORISATION - 220V

| | | |
|---|---|---|
| SONO | AMPLIFICATEUR SONORE AVEC MICROPHONE (Timonerie) | 1 u |
| | HAUT-PARLEUR - IP20 | 3 u |
| | HAUT-PARLEUR EXTERIEUR - IP55 | 2 u |

## LUTTE INCENDIE

| | | |
|---|---|---|
| | EXTINCTEURS CO2 - 2 kg | 5 u |
| | EXTINCTEURS EAU PULVERISEE - 6 kg | 5 u |
| | EXTINCTEURS FIXES GAZ NOVEC avec tirette manuelle de commande à distance sur pont - bonbonne 30 kg (Cpt-machine-AR) - bonbonne 16 kg (Cpt-Machine-AV) | 2 u |
| SSI | SYSTEME DE SECURITE INCENDIE - ALARME Type-3 DECLENCHEURS MANUELS + BLOC AUTONOME ALARME SONORE | 1 u |
| DMA | DECLENCHEUR MANUEL D'ALARME SONORE | 5 u |
| BAAS | BLOC AUTONOME D'ALARME SONORE | 4 u |
| DAI | DETECTEUR AUTOMATIQUE D'INCENDIE dans Cpt-MACHINE ARRIERE & AVANT | 2 u |

**PLAN PRELIMINAIRE**
Transmis le : 12/ 03/ 2014
A : TECHNI-France
Pour : EXAMEN/VALIDATION

| | |
|---|---|
| UNITE mètre | N°PLAN EPD/2014/BC/**PE** |
| ECHELLE A.D (Imp-A3) | INDICE A - 12/ 03/ 2014 |
| DATE 02/ 2014 | CLIENT Mme Anne SAINT-PRIX |

COPYRIGHT - TECHNI CARENE - 2014
TOUS DROITS RESERVES

**Bateau à Passagers Fluvial**
**Refonte Péniche Freycinet**
**Madame Anne SAINT-PRIX**

Bateau Chocolaté

**Etude de Projet Détaillé-EPD**

# INCENDIE

**Techni Carène** ARCHITECTURE & INGENIERIE NAVALES
6, Route de Bû - Les Christophes - 28260-SOREL-MOUSSEL - FRANCE
Tél:02.37.41.80.38 E.Mail: techni-carene@wanadoo.fr Site web: www.techni-carene.com